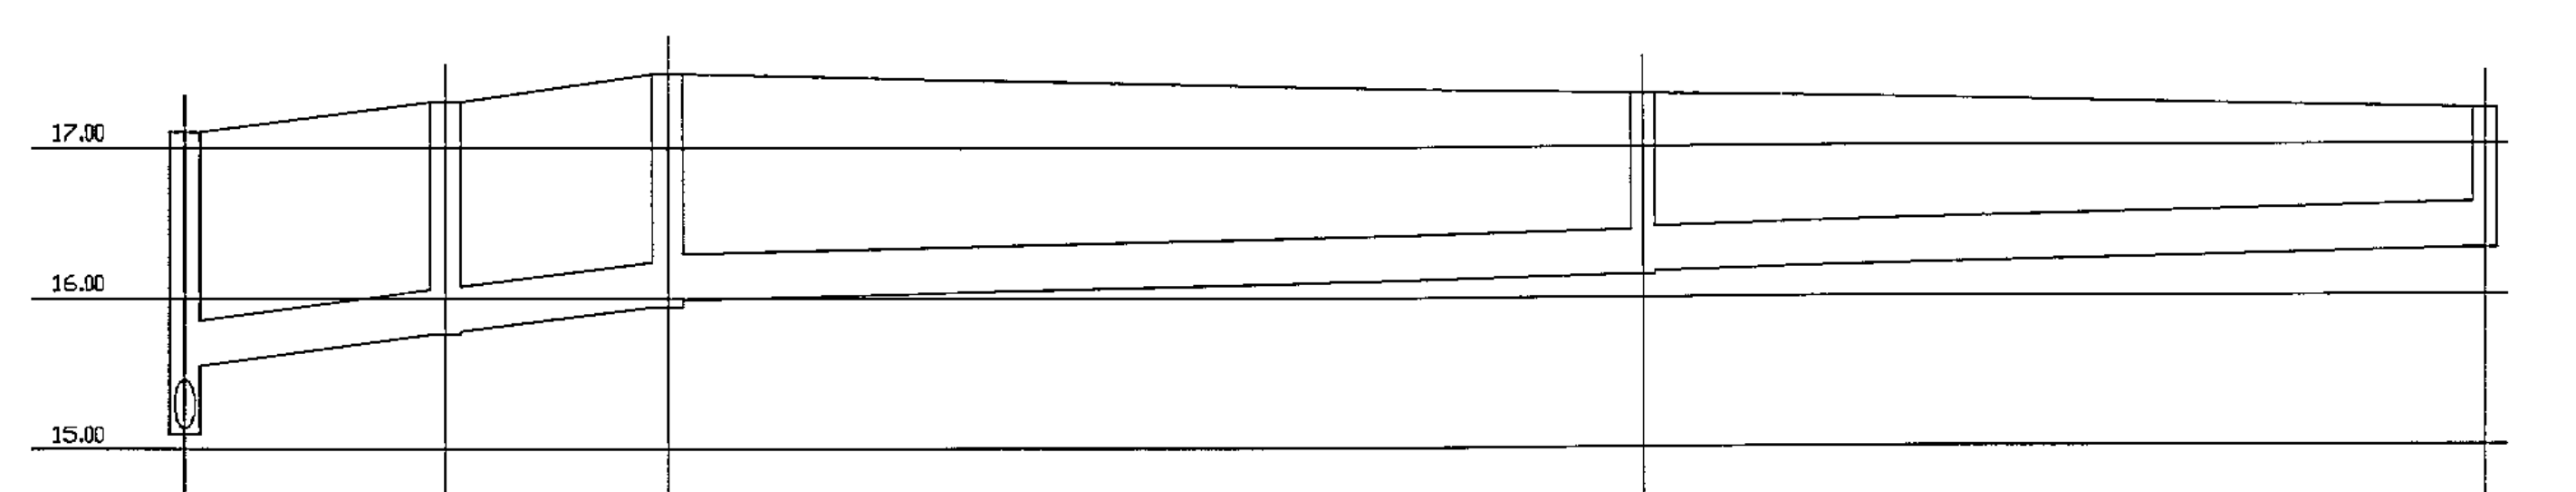

מספר התא בקרה	N1 תא עירוני	N2	N3	N4	N5
מרחק בין התאים		8.60	7.30	31.90	27.40
מרחק מסוכם	0.00	8.60	15.90	47.80	75.20
(TL) רום פני המיכסה (GL) רום פני הקרקע	17.10	17.30	17.49	17.35	17.23
(IL) רום תחתית הצינור	15.50 15.55	15.76 15.78	15.94 15.99	16.15 16.17	16.31 16.33
(H) עומק תחתית הצינור	1.60 1.55	1.54 1.52	1.55 1.50	1.20 1.18	0.92 0.90
שיפועי חומר וקוטר הצינור		2.7% ø300mm	2.6% ø300mm	0.5% ø300mm	ø300mm

File: P:\ShevetHaNasi\Nikuz
Drawing: P:\ShevetHaNasi\Plmb-ShevetHaNasi.dwg
Date: 04/01/11

חתך לאורך הניקוז

(1: 250 1: 50)

פרט תעלת ניקוז

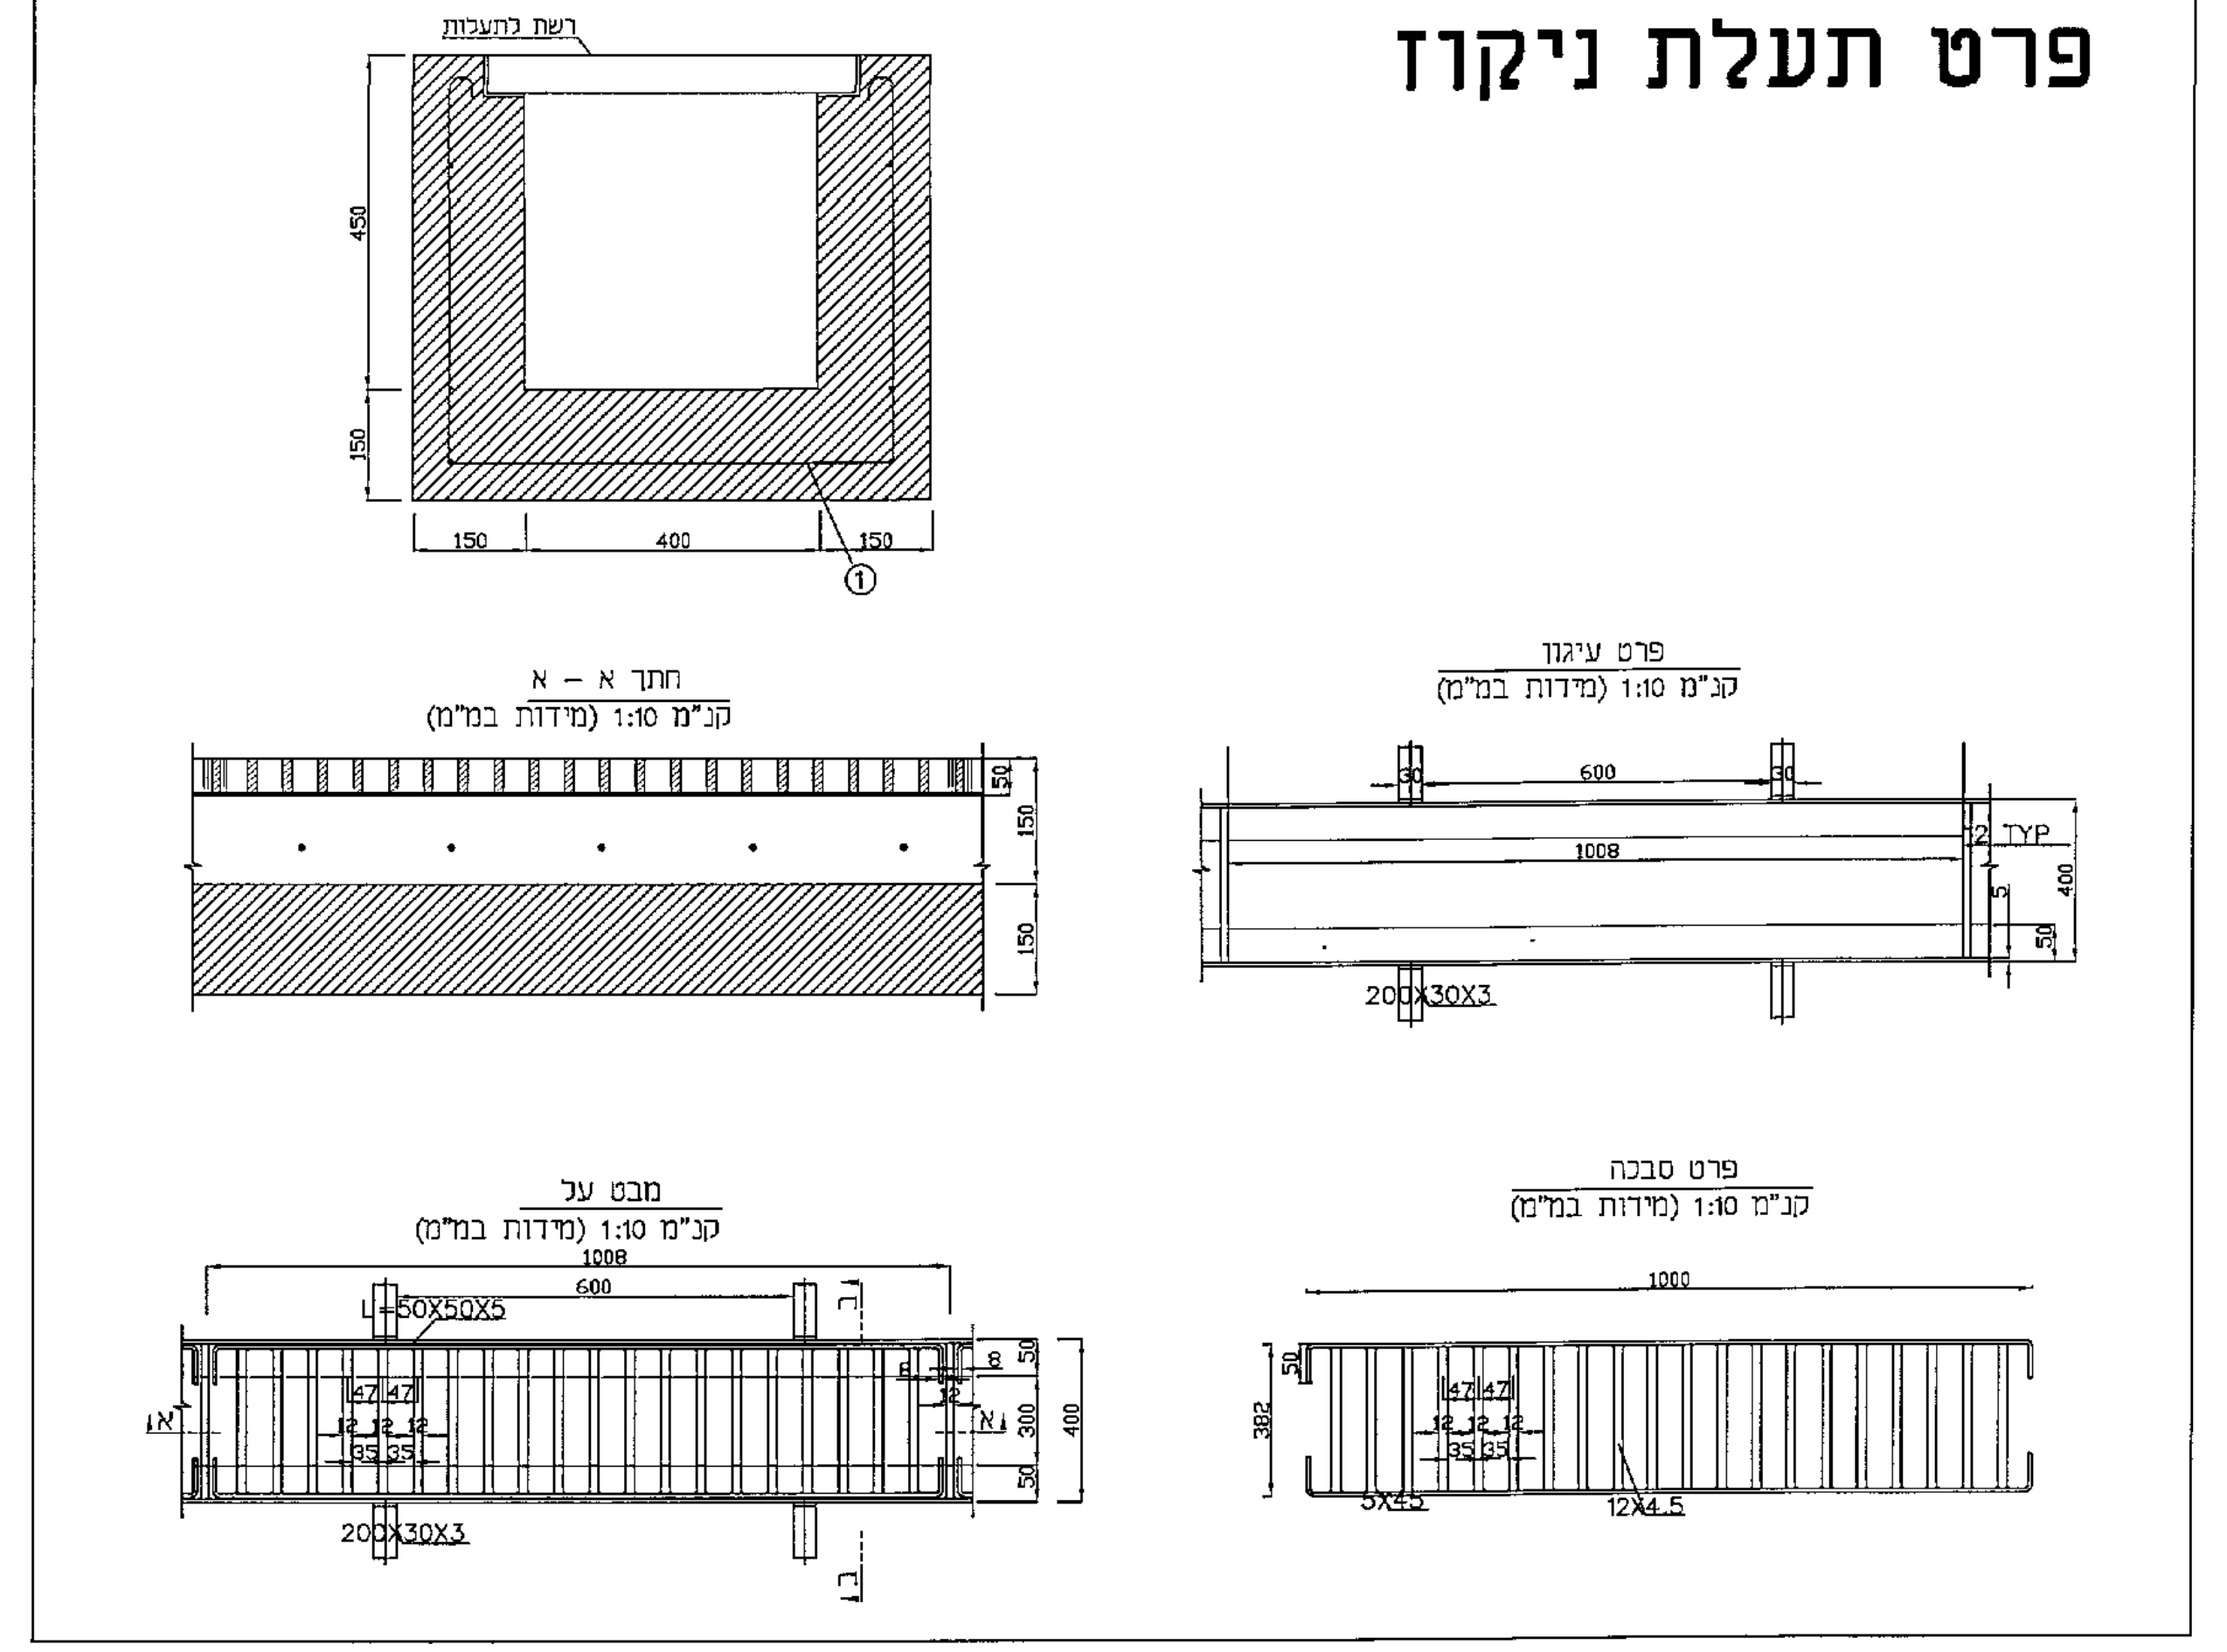

מפה טופוגרפית

קנה מידה : 1 : 250

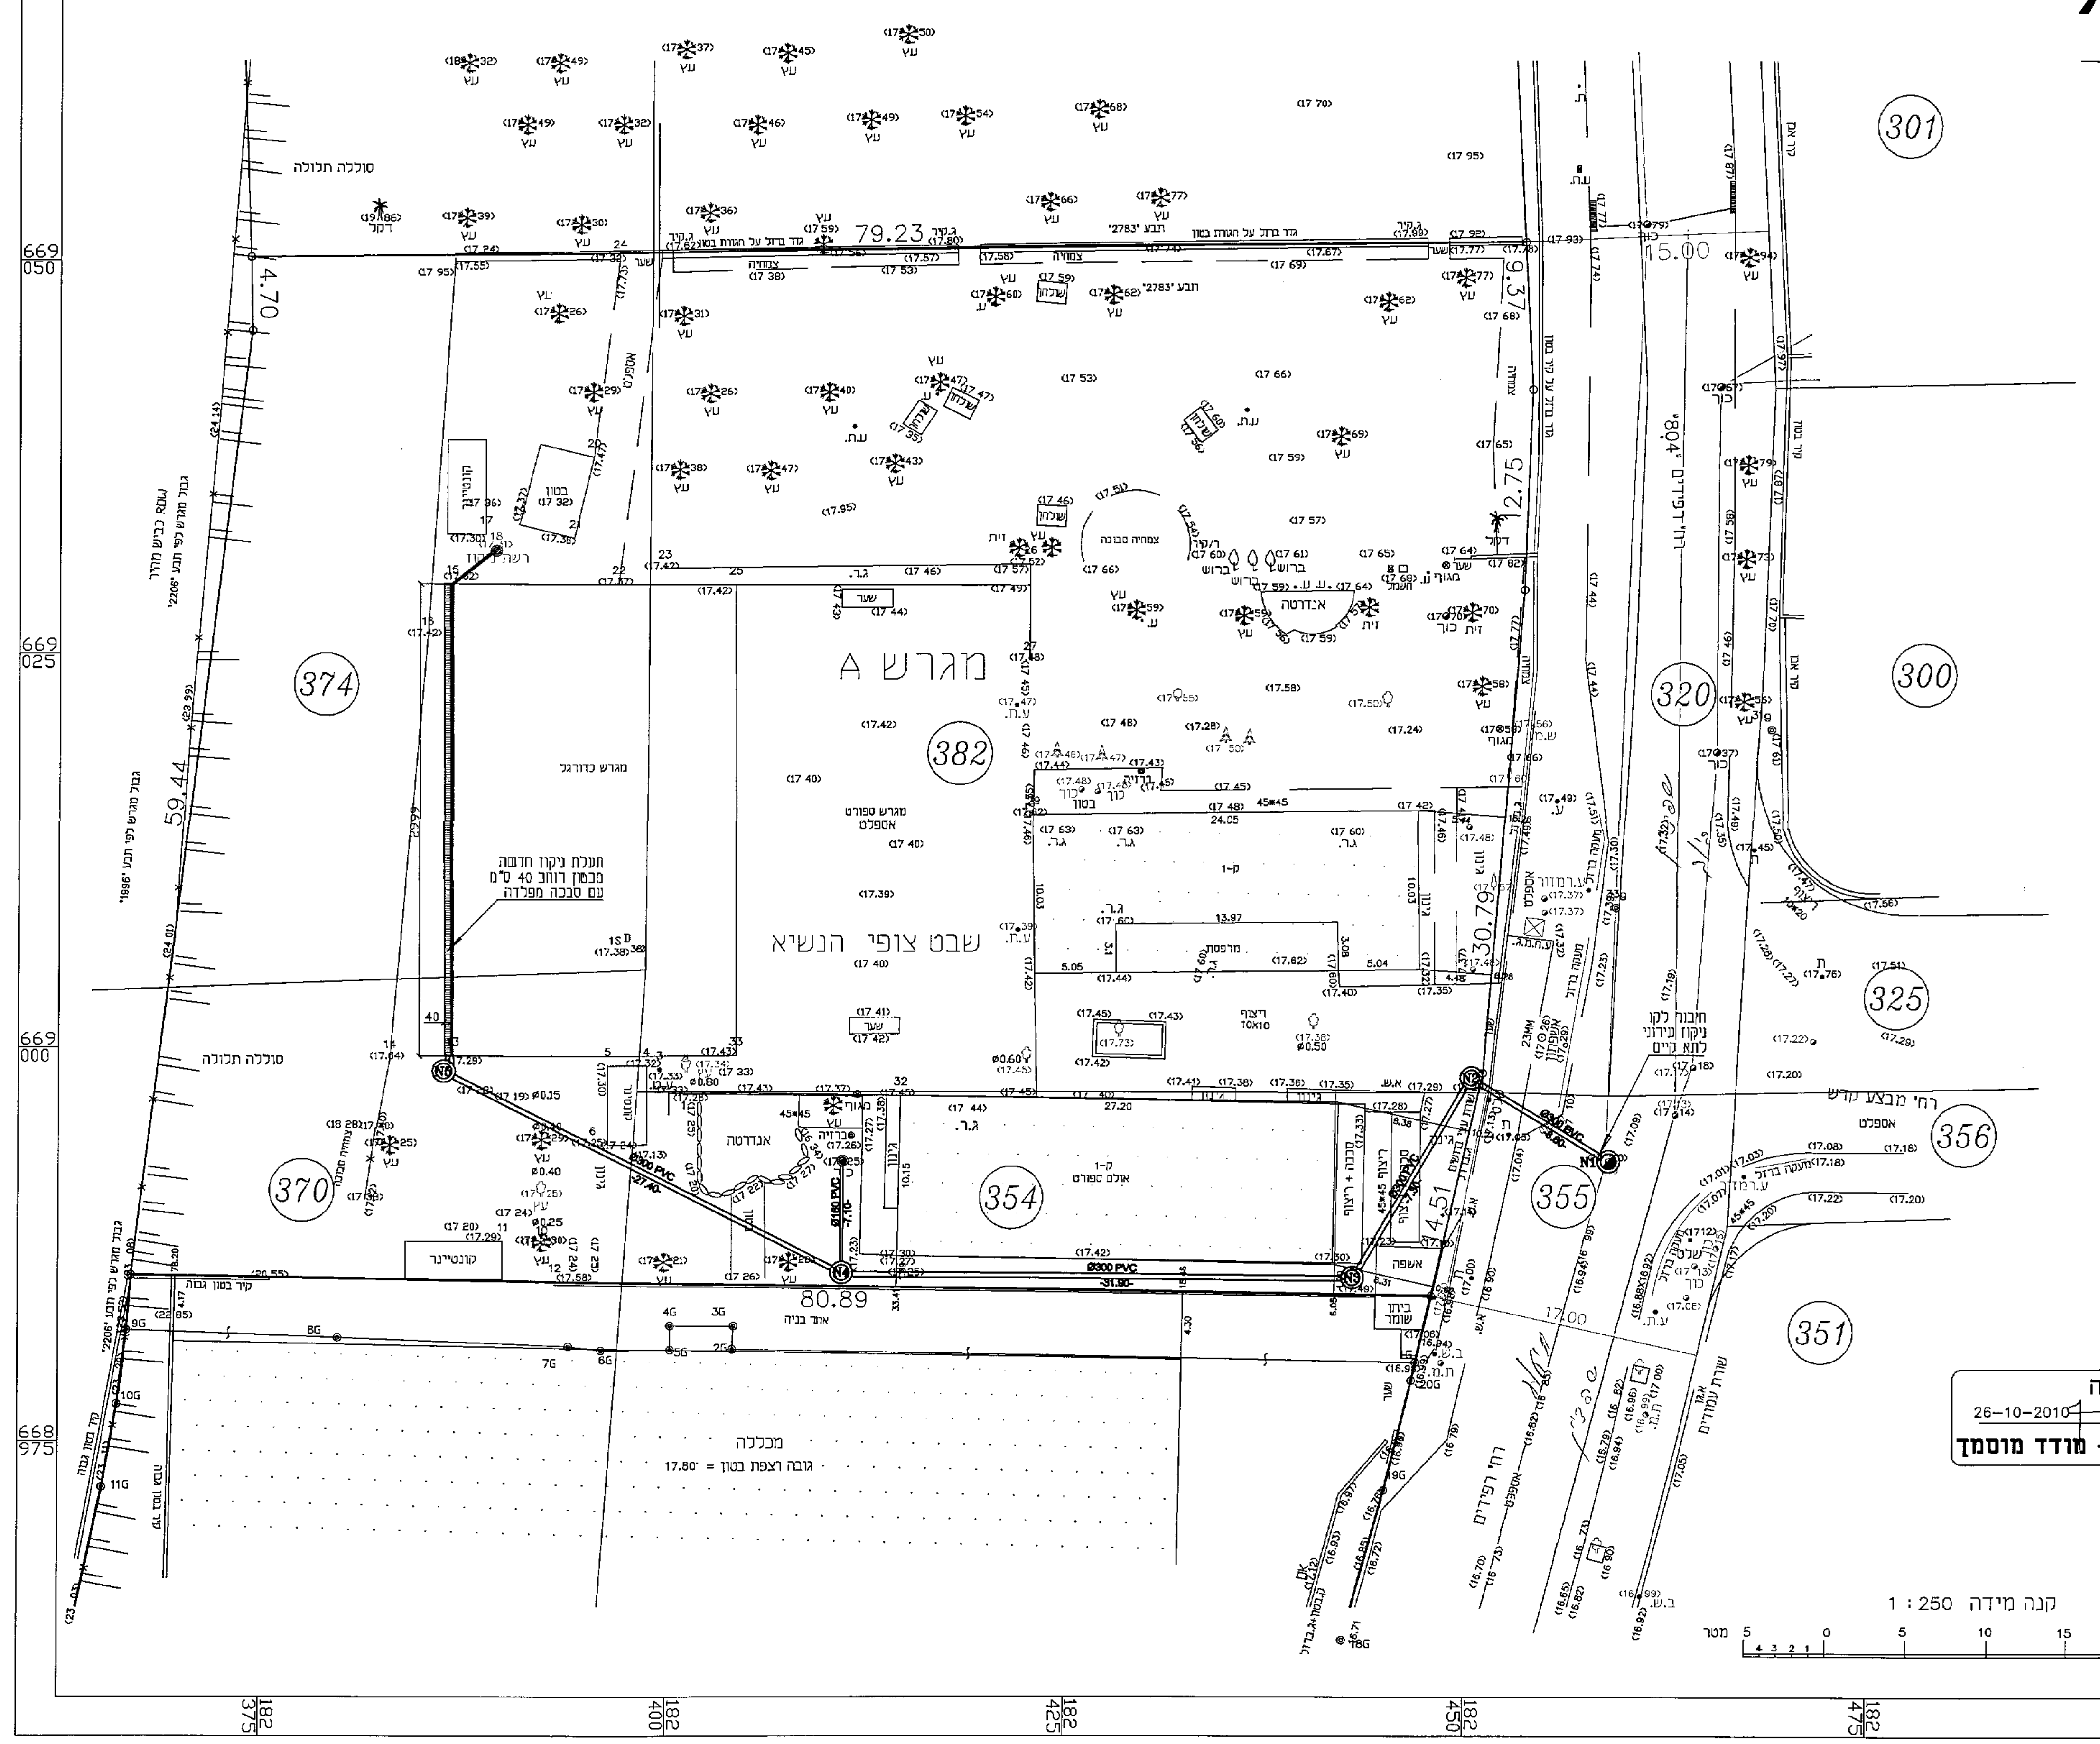

מקום : תל-אביב
מחוז : תל-אביב
נפה : תל-אביב – יפו
גוש : 6627
חלקי חלקות : 354, 370, 374, 382
מגרש : "A"
שטח המגרש : 5,349 ד"מ

הוכן עבור : מוסדות חינוך
לצורך : היתר בניה

תרשים סביבה

קנה מידה : 1 : 1250

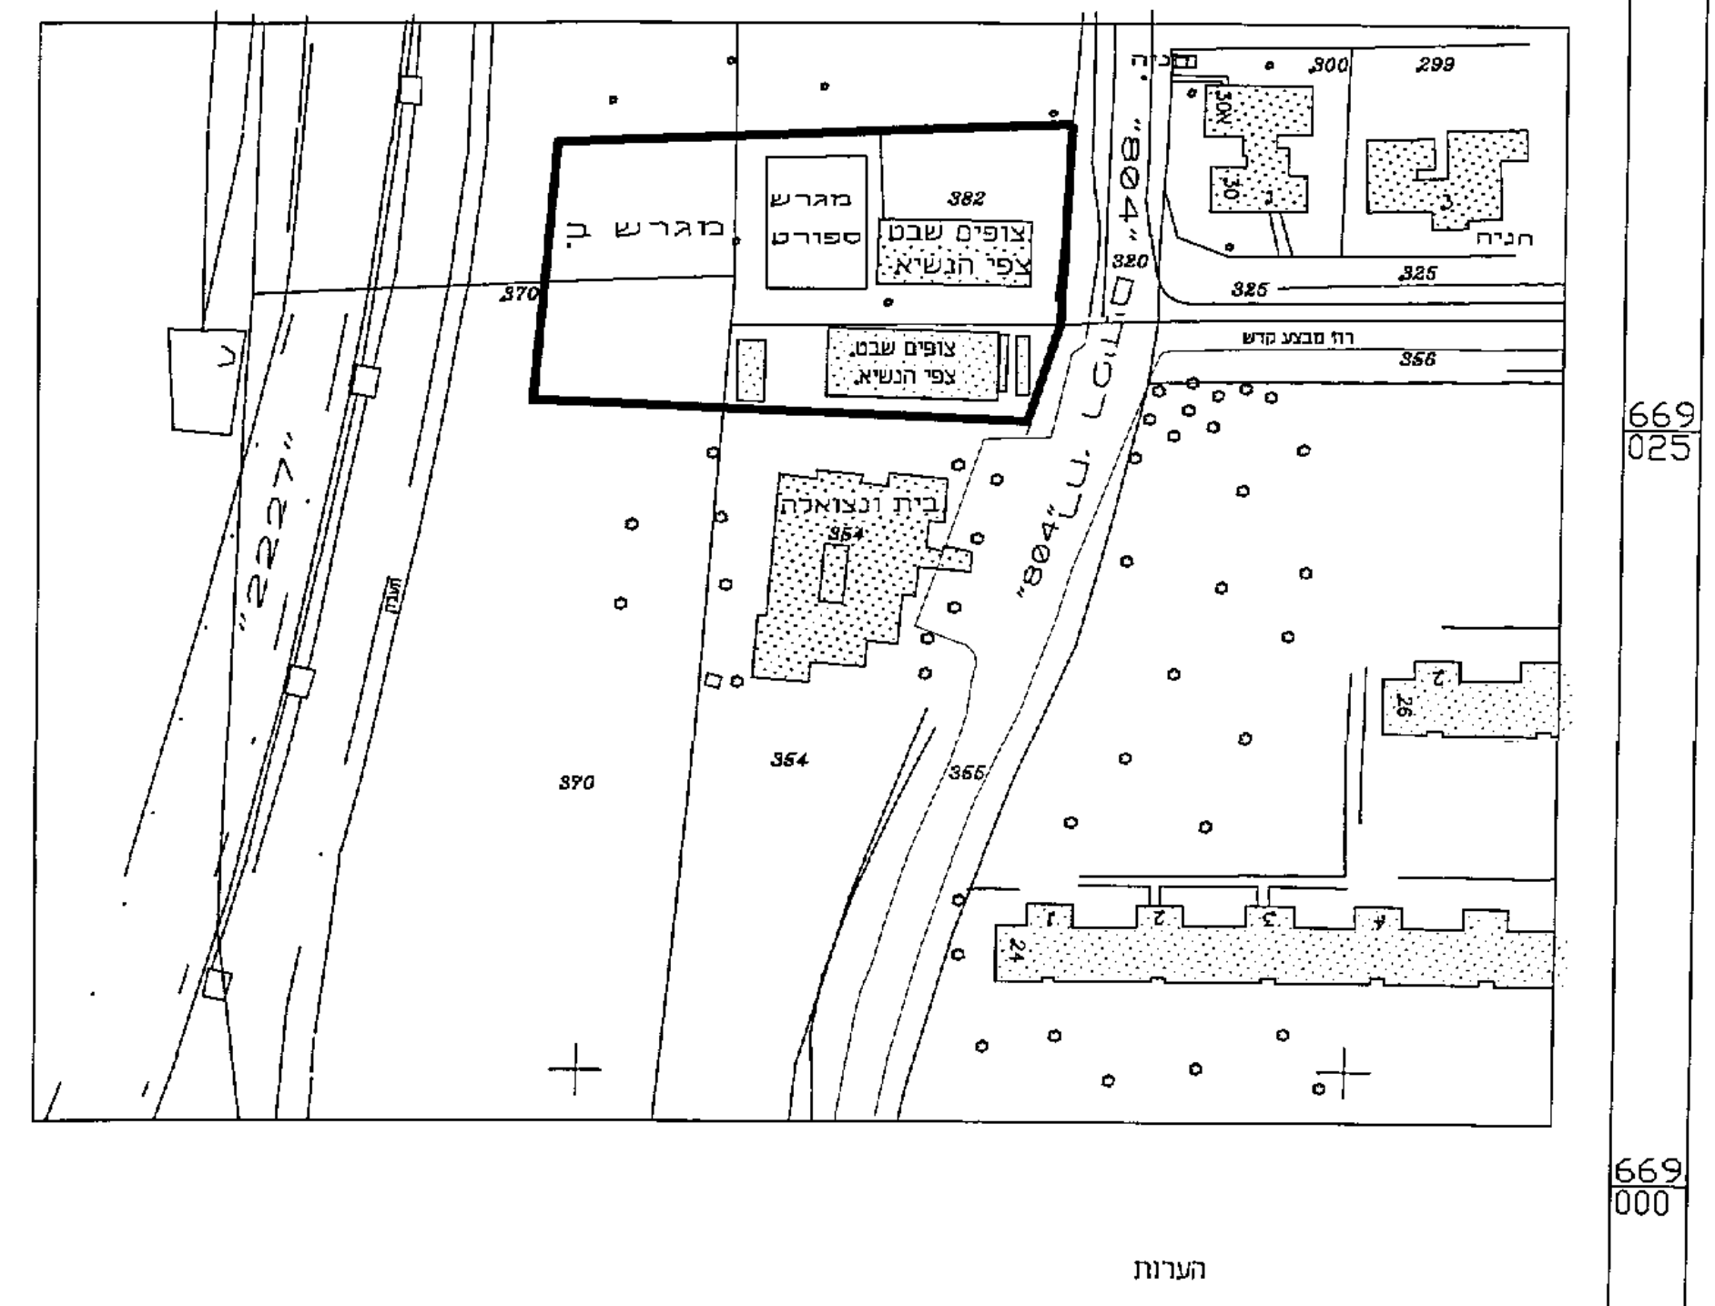

הערות

1. הגבהים מבוססים על נ.ק.313 של ע.ת.א.
   שגובהה : 19.525 מ'
2. גבולות המגרש הדרומי והמערבי נלקחו מהמפה שהוכנה ע"י המודד עבור
3. גבול המגרש הצפוני קבתי לפי גדר רשת קיימתי
   גבול המגרש המזרחי הינו קו הדרך של רחוב רפידים
4. התכנית תואמת תב"ע 2206 של נתיבי איילון
5. גבולות מגרש סופיים יקבעו לאחר אישור
   מחלקת המדידות של ע.ת.א ונתיבי איילון.

המפה עודכנה בתאריך 26-10-2010

דרור בן נתן – מודד מוסמך

לא לצרכי רישום !

חתימה	רשיון	תאריך
	594	07-02-2007

דרור בן נתן – מודד מוסמך

רחוב יצחק שדה 34 תל אביב 0526-344759 03-5374395

		תאריך
	מוסדות חינוך	
	1	4.1.11

	שם	תאריך

הקבלן אחראי לבדיקת המידות שבתכנית. על כל טעות, סטיה או אי התאמה עליו להודיע למתכנן. אין לקבוע מידות ע"י מדידה בשרטוט אלא באישור המתכנן.
התכנית הנה רכוש הבלעדי של המתכנן ובעלותו מוגנת ע"י חוק זכויות היוצרים.
אין לעשות כל שימוש בתכנית זו וברעיונות הגלומים בה ללא אישור מראש ובכתב של המתכנן.

● לעיון ○ למכרז ○ לבצוע

א. יצהר
שרותי הנדסה
רח' צבי ברגמן 7, א"ת סגולה פ"ת 49279
טל: 03-9344180 פקס: 03-9344185
www.izhar.co.il aizhar@izhar.co.il

תכנון זה נעשה תחת בקרה של מערכת נהול איכות העומדת בדרישות ISO 9001:2008 מאושרה ע"י BVQI/IQC תעודה מס' 4534

שם הפרויקט:

הסדרת ניקוז במגרש צופי שבט הנשיא

שם הגליון:

תנוחה כללית וחתך לאורך קו ניקוז

מס' הפרויקט:	מס' הבנין:	מס' הגליון:	תאריך:
760		1	3.1.11

ק.מ.:	מהדורה	תאריך עדכון:	סה"כ גליונות:	מידות הגליון:
1:250 1:250/50	0		1	700X1800

תכנן:	שרטט:	בקר:	אישר:	תאריך:
א.יצהר	לריסה ש.		א.יצהר	

שם הקובץ במחשב: P:\ShevetHaNasi\Plmb-ShevetHaNasi.dwg

---

008 23

אין התנגדות 16.01.2011 תאריך

עיריית תל – אביב – יפו
מינהל ההנדסה , אגף רישוי ופיקוח על הבנייה
שדרות בן-גוריון 68 תל-אביב 64514 (פקס 5231340) טלפון 5217120, 5217045

לכבוד ☐ הועדה המקומית לתכנון ולבנייה
☐ רשות הרישוי המקומית

חוק התכנון והבניה, התשכ"ה-1965
תקנות התכנון והבנייה (בקשה להיתר תנאיו ואגרות) התש"ל-1970

בקשה להיתר בנייה או לשימוש במקרקעין – בניין חדש

יש להקפיד למלא את כל הפרטים בטופס הבקשה ולצרף מסמכים כמפורט ברשימת התיוג המצורפת

על פי טופס 1 תקנה 2(א)

מס' תיק הבניין	מס' בקשה קודמת להיתר בנייה	מס' הבקשה למידע	מתאריך

א. פרטי הנכס והמבקשים

הכתובת	רחוב	מס' בית	גוש	חלקה	תת חלקה	מגרש	הוראות התכניות החלות על המקום
	רפידים	29	6627	382,374,370,354		A	

פרטים אישיים	שם משפחה שם פרטי / שם חברה או תאגיד	מס' זהות/חברה או מס' רישום תאגיד	רחוב ומספר בית / ישוב ומיקוד	מספר טלפון / מספר פקס
מבקש 1	חב' מוסדות חינוך ותרבות בתל אביב	ח.פ 510623721	רח' אידלסון 29 תל אביב	03-5254241 03-5254974
מבקש 2				
מבקש 3				
בעל הזכות בנכס	חב' מוסדות חינוך ותרבות בתל אביב	ח.פ 510623721	רח' אידלסון 29 תל אביב	03-5254241 03-5254974
החוכר				
עורך הבקשה הראשי	א. יצהר שרותי הנדסה	ח.פ 513769752	רח' צבי ברגמן 7 א"ת סגולה פ"ת	03-9344180 03-9344185
מתכנן שלד הבניין				

ב. מהות הבקשה לבניה חדשה

☐ הריסת מבנה קיים הכולל ____ קומות מגורים/ ____
☐ הקמת מבנה חדש הכולל:
☐ מרתף/ים ☐ קומה מפולשת ☐ קומה מסחרית ל ____
☐ ____ קומות מגורים ובהן ____ יחידות דיור משרדים
☑ **הסדרת ניקוז במגרש וחיבור לתיעול עירוני**
☐ המרתף/ים כולל/ים: ☐ מקלט ☐ מחסן ☐ חדרי עזר ____
☐ קומת הקרקע כוללת: ☐ אולם כניסה ☐ חדר גז ☐ חדר אשפה ☐ ____ חנויות ☐ מסעדה ☐ ____ חדרי שירותים ☐ ____
☐ על הגג: ☐ חדרי יציאה ☐ חדרי מכונות ☐ קולטי שמש ☐ חדר מדרגות כללי ☐ פרגולה ☐ ____
☐ בחצר: ☐ ____ מקומות חנייה ☐ גינה ☐ שטחים מרוצפים ☐ פרגולה
☐ בגבולות המגרש גדר בגובה ____ מטר
פירוט נוסף: ____

ג. מפרט – תיאור הבקשה

תיאור הקיים על המגרש: מתנה צופים שבט הנשיא

שימוש עיקרי: ☐ מגורים ☐ משרדים ☐ מסחר ☐ מלונאות ☐ בידור ☑ נופש וספורט ☐ תעשייה ☑ בניין ציבורי ☐ מלאכה ☐ חקלאי ☐ שימוש אחר, פרט:

סוג העבודה או השימושים המוצעים: ☐ הריסה ☐ בניין חדש

הגורם שמתבצעת בעבורו הבנייה: ☐ משרד ממשלתי ☐ רשות מקומית ☐ מוסד ציבורי ☐ גורם פרטי ☐ בנה ביתך ☐ אחר:

שטחים: שטח הבנייה הכולל המבוקש מ"ר; שטח המגרש/החלקה מ"ר; אחוזי הבנייה %

ד. חומרי הבניה

סוג הבנייה: ☐ רגילה ☐ בית מוכן ☐ מתועשת ☐ אחר
קירות חיצוניים: ☐ בטון מזוין ☐ בלוקים ☐ אבן טבעית ☐ לבנים שרופות ☐ אחר
חומרי גימור: ☐ אבן מלאכותית ☐ אבן טבעית ☐ טיח ☐ זכוכית ☐ אחר
תקרות: ☐ בטון מזוין ☐ עץ ☐ אחר
גג: ☐ בטון מזוין ☐ רעפים ☐ אסבסט ☐ פח ☐ אחר
גדרות: ☐ אבן טבעית ☐ אבן מלאכותית ☐ בטון ☐ בלוקים ☐ ברזל ☐ עץ ☐ רשת ☐ אחר
קיימות ____ מ"א מוצעות ____ מ"א סה"כ ____ מ"א

ה. השטחים המבוקשים לבנייה (על-פי תכני ת הבנייה) והמותרים לבנייה (על-פי "אסמכתא": חוק , תקנות , תכנית) בכל מפלס בנפרד ולפי שימוש

ו. קווי בנייה

ת. פרטי הבנייה – לשימוש הלשכה המרכזית לסטטיסטיקה

הייעוד		מספר חדרים	מספר דירות	מספר מגורים
למגורים	1			
להארחה	2			
לעסקים ולמשרדים	3			
לבנייני ציבור	4			
לתעשייה ולמלאכה	5			
למשק חקלאי	6			
למקלט או למרתף				
למבני עזר				
סך כל שטח הבנייה	סה"כ			

ט. הבקשה מוגשת לאישור
☐ הוועדה המקומית
☐ רשות הרישוי המקומית
☐ רשות הרישוי המקומית באמצעות מורשה להיתר

יא. חתימות נוספות

יב. מינויים מטעם מבקש ההיתר – נתמנה אדם אחד ליותר מתפקיד אחד, ימולאו פרטיו ליד כל אחד מהתפקידים שהוא ממלא על פי הוראות כל דין.

מינוי עורך הבקשה הראשי: אני ממנה בזה את אלכס יצהר בעל/ת מס' זהות 016498370 הרשום בסעיף א להיות עורך הבקשה הראשי להיתר, ולייצגני לפני מוסדות התיכנון והרשויות המוסמכות בכל הנוגע לטיפול בבקשה להיתר ולקבלתו, לרבות התיקונים בכל שידרשו הרשויות המוסמכות.

מינוי עורכי בקשה לפי תחומים:

שם משפחה ושם פרטי	תחום פעולה	המען	מספר טלפון	מספר פקס
1. אלכס יצהר	מתכנן האינסטלציה הסניטרית	צבי ברגמן 7 פתח תקווה	03-9344180	03-9344185
2.				
3.				

יג. הצהרות

	תאריך	שם משפחה ושם פרטי	מספר רישיון	חתימה
עורך בקשה ראשי				
עורך בקשה 1 מתכנן האינסטלציה הסניטרית	11.1.11	אלכס יצהר	23763	
עורך בקשה 2				
עורך בקשה 3				